

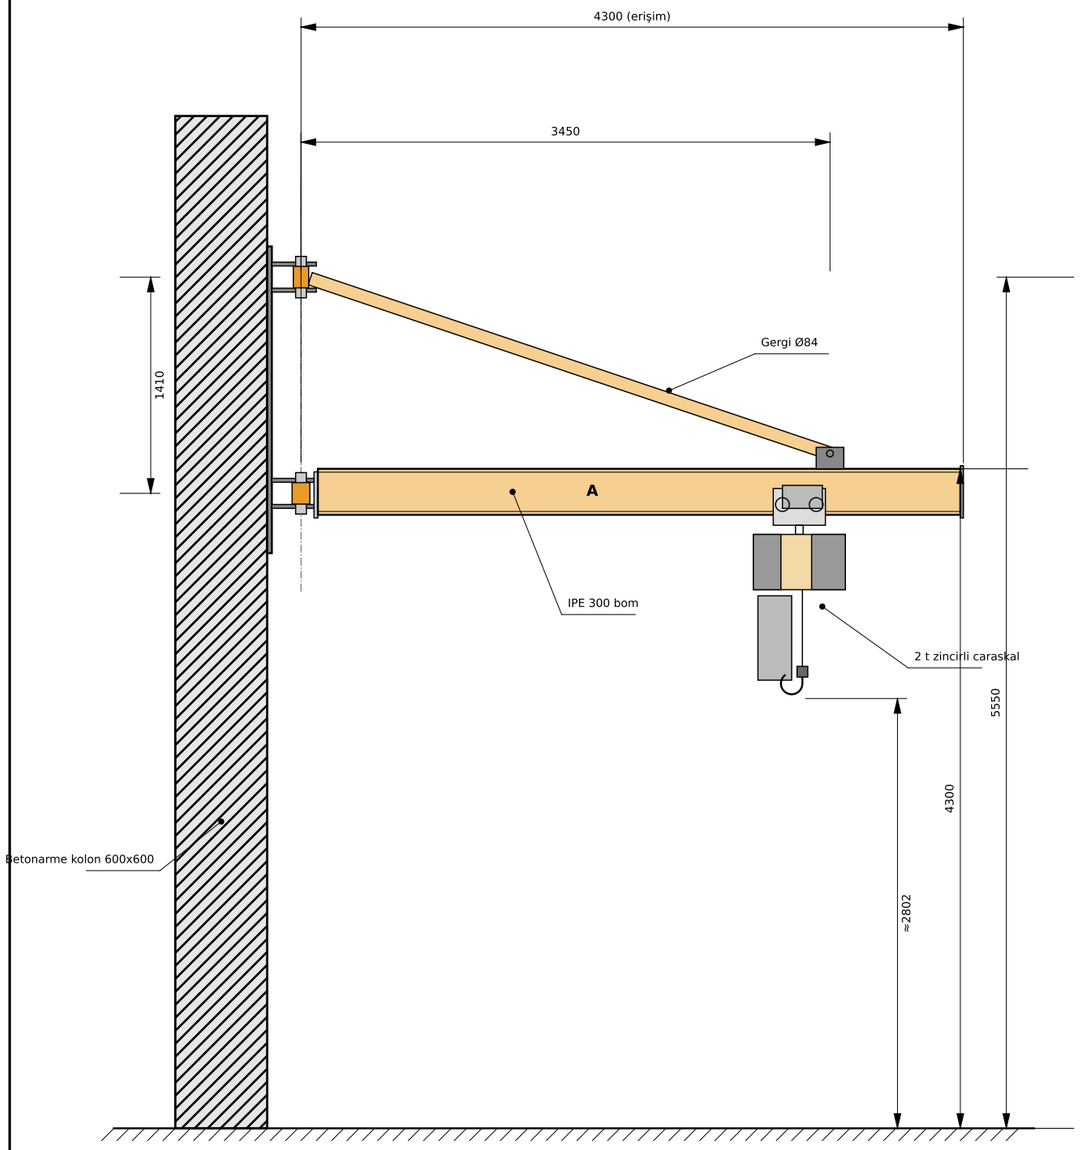


ÖN GÖRÜNÜŞ
Ölçek 1:40

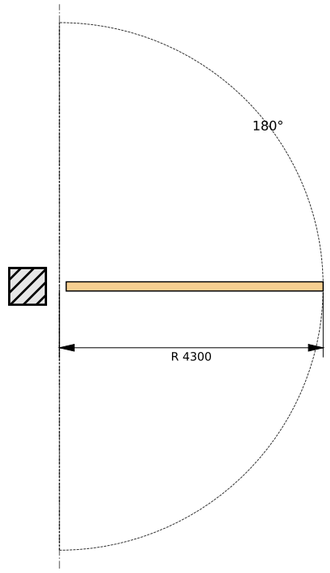

PLAN
Ölçek 1:100

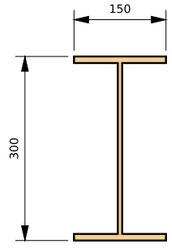


IPE 300 tf=10,7 tw=7,1

A-A KESİTİ (BOM)
Ölçek 1:10


NOTLAR

1. Bom IPE 300 (S355JR), üstten gergili; alt flanş caraskal yürüyüş yolu olarak serbesttir.
2. Konsol: 30 mm taban levhası, her mafsalda 25 mm alt/üst kulak levhası + guse, Ø70 dikey pim.
3. Gergi Ø84 boru, gerdirme manşonlu; bom üst flanşında pimli kulak (x = 3450).
4. Dönme açısı 180°. Festoon C rayı bom yanında, üst flanş altında.
5. Bina kolonu 600x600 betonarme; konsol 8 adet ankraj cıvatası ile bağlanır (ölçüler projede).


beta VİNÇ SİSTEMLERİ	ÇİZİM ADI: **DUVAR TİPİ PERGEL VİNÇ**		
	KAPASİTE: **2 t (zincirli caraskal)**		
ÖLÇEK: **1:40 / 1:100 / 1:10**	ÖLÇÜ BİRİMİ: **mm**	TARİH: **18.10.2026**	PAFTA NO: **BV-PV-01**
MALZEME: **S355JR yapı çeliği (taşıyıcılar)**		YÜZEY: **Boya RAL 1028 tonu / RAL 7016**	
Görselleştirme modelinden türetilmiştir. İmalat ve statik hesap için onaylı proje esas alınır.			

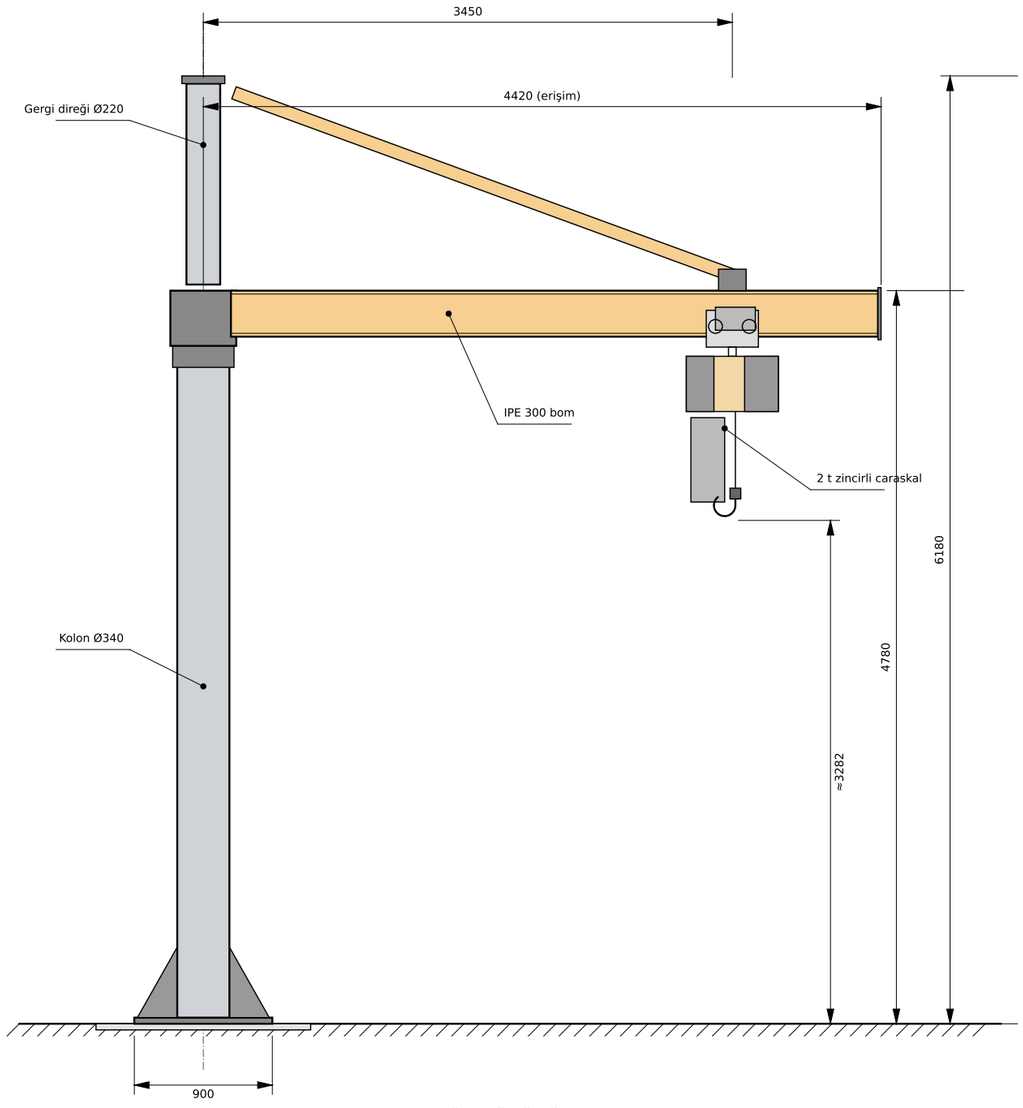

ÖN GÖRÜNÜŞ
Ölçek 1:40

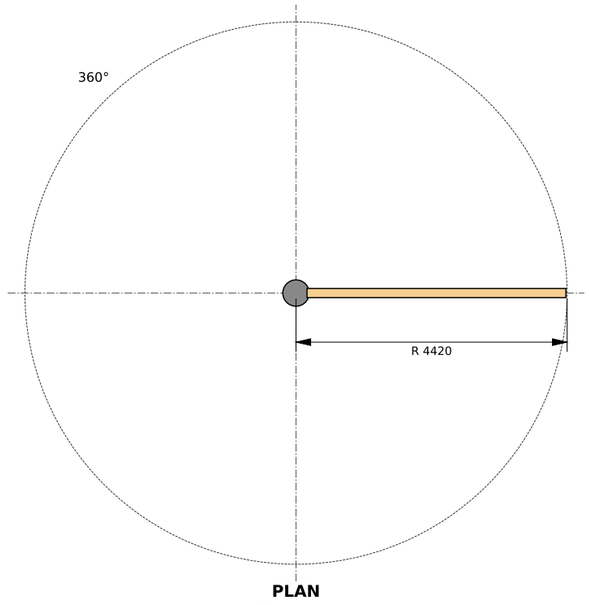

PLAN
Ölçek 1:100

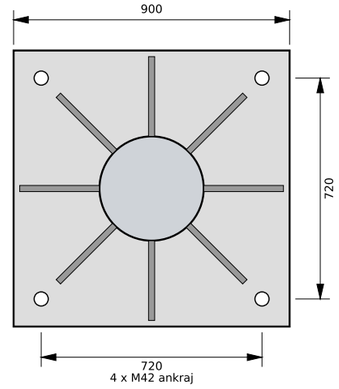

TABAN LEVHASI
Ölçek 1:20


NOTLAR

1. Kolon Ø340 boru (S355JR), taban levhası 900x900x40, 8 guse, 4 ankraj (M42) 720x720 aks.
2. Dönen başlık Ø430, üstünde Ø220 gergi direği; gergi Ø84, bom üst flanşında pimli kulak.
3. Bom IPE 300, üstten gergili; alt flanş caraskal yürüyüş yolu olarak serbesttir.
4. Dönme açısı 360°. Festoon C rayı bom yanında.
5. Temel boyutları zemin etüdüne göre statik projede belirlenir.


beta
VİNÇ SİSTEMLERİ

ÇİZİM ADI: **KOLON TİPİ PERGEL VİNÇ**			
KAPASİTE: **2 t (zincirli caraskal)**			
ÖLÇEK: **1:40 / 1:100 / 1:20**	ÖLÇÜ BİRİMİ: **mm**	TARİH: **18.10.2026**	PAFTA NO: **BV-PV-02**
MALZEME: **S355JR yapı çeliği (taşıyıcılar)**		YÜZEY: **Boya RAL 1028 tonu / RAL 7016**	


Görselleştirme modelinden türetilmiştir. İmalat ve statik hesap için onaylı proje esas alınır.

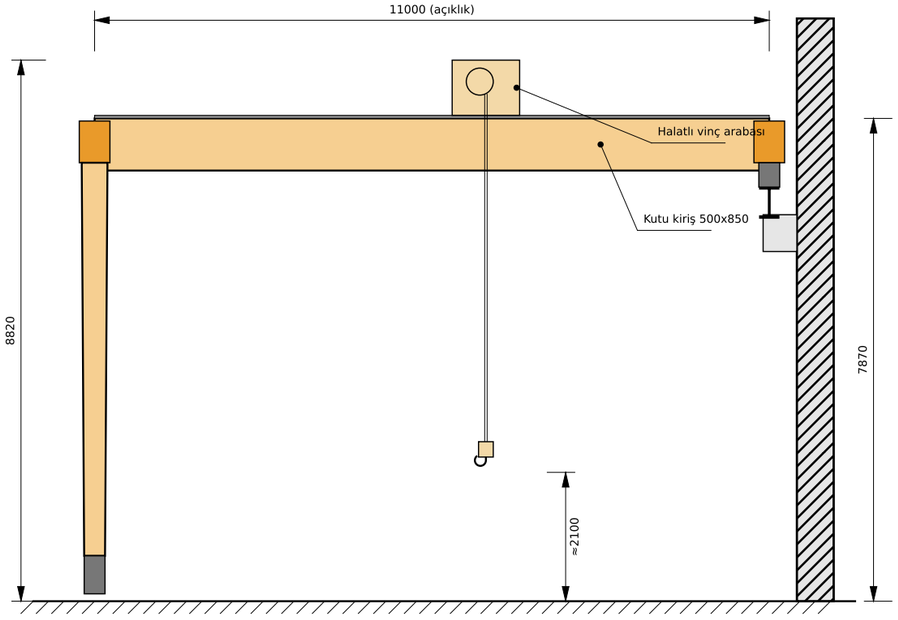

ÖN GÖRÜNÜŞ
Ölçek 1:100

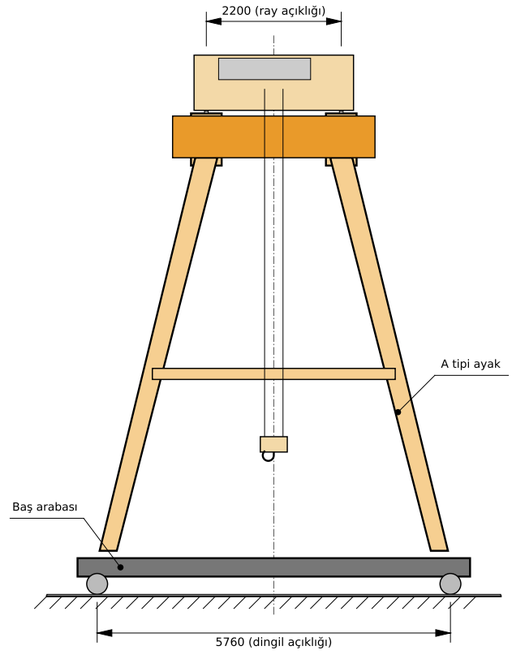

YAN GÖRÜNÜŞ (AYAK TARAFI)
Ölçek 1:100

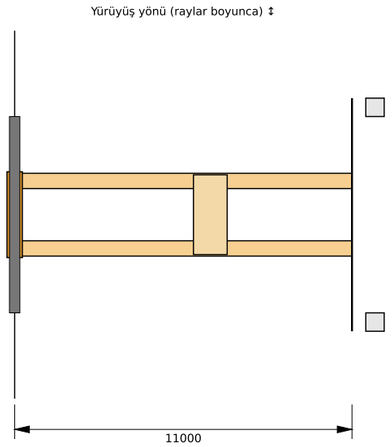


PLAN
Ölçek 1:200


NOTLAR

1. Bir uç A tipi ayaklarla zemin rayında, diğer uç bina kolonu konsolundaki yürüyüş yolu kirişinde.
2. Ana kirişler 2 x kutu kiriş 500x850 (S355JR), uç kirişlerle cıvatalı birleşim.
3. Yürüyüş yolu kirişi bina kolonu konsollarına oturur; kolon ve konsol ölçüleri bina projesinde.
4. Halatlı vinç arabası iki kirişin üstündeki raylarda yürür; enerji festoon sistemiyle.
5. Ray sonlarında stoper ve tampon; ayakta merdiven ve kablo tamburu.


beta VİNÇ SİSTEMLERİ	ÇİZİM ADI **ÇİFT KİRİŞLİ YARI PORTAL VİNÇ**		
	KAPASİTE **— (projeye göre)**		
ÖLÇEK **1:100 / 1:200**	ÖLÇÜ BİRİMİ **mm**	TARİH **18.10.2026**	PAFTA NO **BV-PV-04**
MALZEME **S355JR yapı çeliği (taşıyıcılar)**		YÜZEY **Boya RAL 1028 tonu / RAL 7016**	
Görselleştirme modelinden türetilmiştir. İmalat ve statik hesap için onaylı proje esas alınır.			

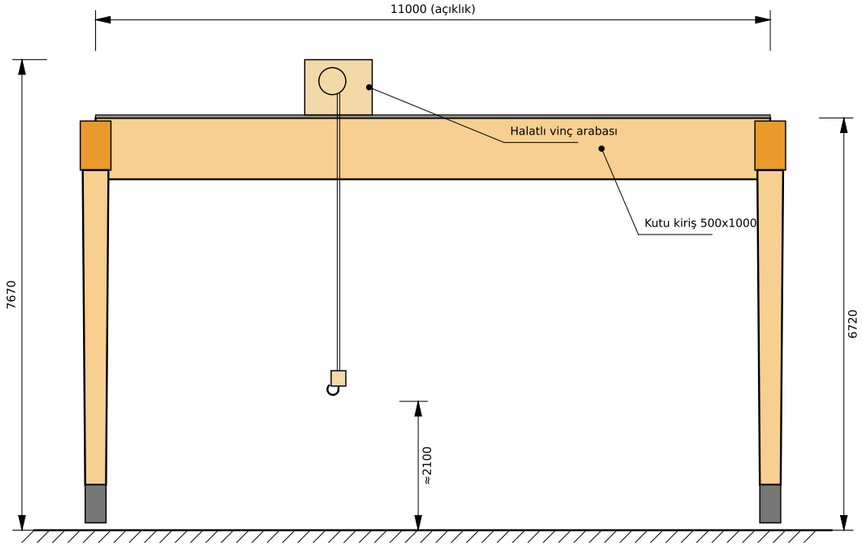

ÖN GÖRÜNÜŞ
Ölçek 1:100

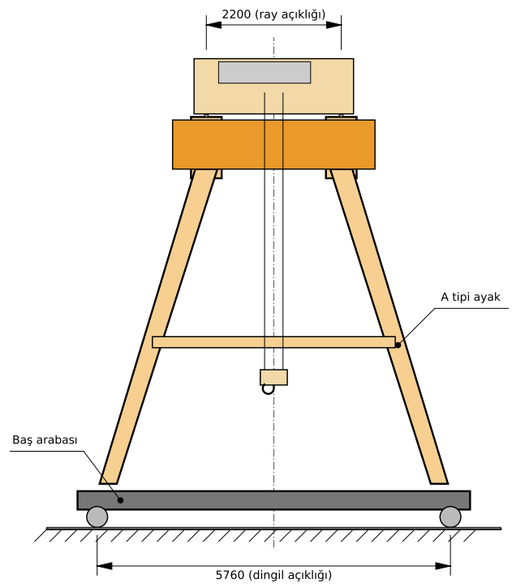

YAN GÖRÜNÜŞ
Ölçek 1:100

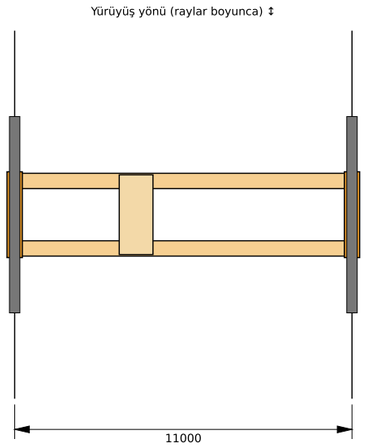

PLAN
Ölçek 1:200

NOTLAR

1. Ana kirişler 2 x kutu kiriş 500x1000 (S355JR), uç kirişlerle alın levhalı cıvatalı birleşim.
2. Her uçta kirişe dik düzlemde A tipi iki ayak; ayak-uç kiriş ve ayak-baş arabası flanşları cıvatalı.
3. Baş arabaları tekerlek bloklu, motor-redüktör-fren tahrikli; raylar kirişe dik doğrultudadır.
4. Halatlı vinç arabası iki kirişin üstündeki raylarda yürür; enerji festoon sistemiyle.
5. Yakın ayakta merdiven ve besleme kablo tamburu; ray sonlarında stoper ve tampon.

beta VİNÇ SİSTEMLERİ	ÇİZİM ADI **ÇİFT KİRİŞLİ PORTAL VİNÇ**		
	KAPASİTE **— (projeye göre)**		
ÖLÇEK **1:100 / 1:200**	ÖLÇÜ BİRİMİ **mm**	TARİH **18.10.2026**	PAFTA NO **BV-PV-03**
MALZEME **S355JR yapı çeliği (taşıyıcılar)**		YÜZEY **Boya RAL 1028 tonu / RAL 7016**	
Görselleştirme modelinden türetilmiştir. İmalat ve statik hesap için onaylı proje esas alınır.			