

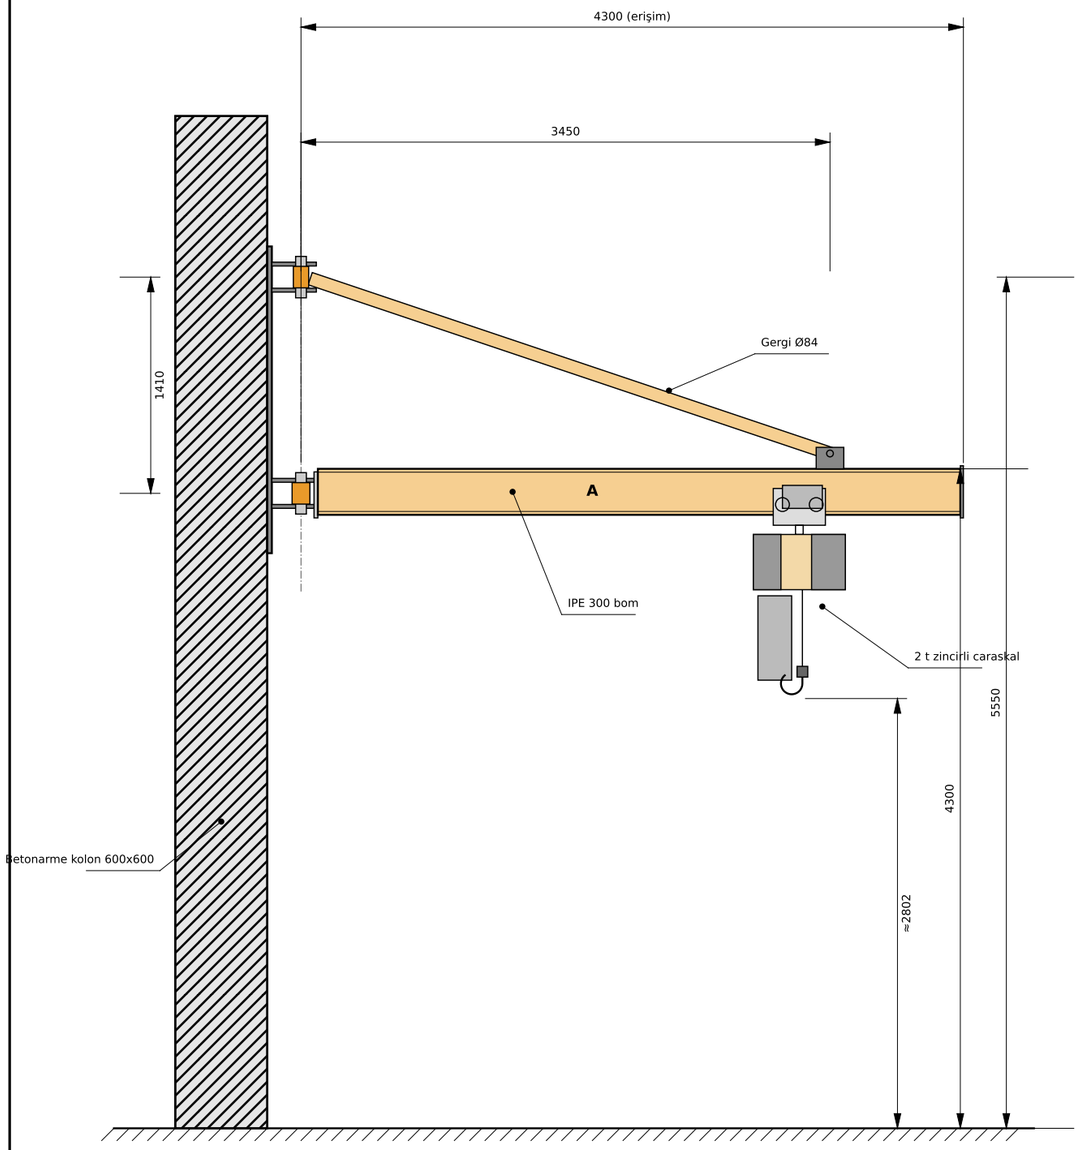


ÖN GÖRÜNÜŞ
Ölçek 1:40

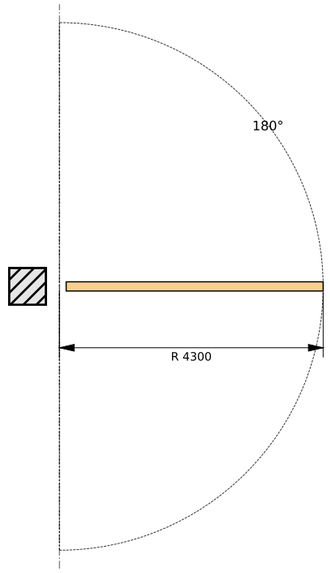

PLAN
Ölçek 1:100

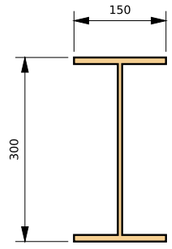

IPE 300 tf=10,7 tw=7,1

A-A KESİTİ (BOM)
Ölçek 1:10

NOTLAR

1. Bom IPE 300 (S355JR), üstten gergili; alt flanş caraskal yürüyüş yolu olarak serbesttir.
2. Konsol: 30 mm taban levhası, her mafsalda 25 mm alt/üst kulak levhası + guse, Ø70 dikey pim.
3. Gergi Ø84 boru, gerdirme manşonlu; bom üst flanşında pimli kulak (x = 3450).
4. Dönme açısı 180°. Festoon C rayı bom yanında, üst flanş altında.
5. Bina kolonu 600x600 betonarme; konsol 8 adet ankraj cıvatası ile bağlanır (ölçüler projede).

beta VİNÇ SİSTEMLERİ	ÇİZİM ADI: **DUVAR TİPİ PERGEL VİNÇ**		
	KAPASİTE: **2 t (zincirli caraskal)**		
ÖLÇEK: **1:40 / 1:100 / 1:10**	ÖLÇÜ BİRİMİ: **mm**	TARİH: **18.10.2026**	PAFTA NO: **BV-PV-01**
MALZEME: **S355JR yapı çeliği (taşıyıcılar)**		YÜZEY: **Boya RAL 1028 tonu / RAL 7016**	
Görselleştirme modelinden türetilmiştir. İmalat ve statik hesap için onaylı proje esas alınır.			