

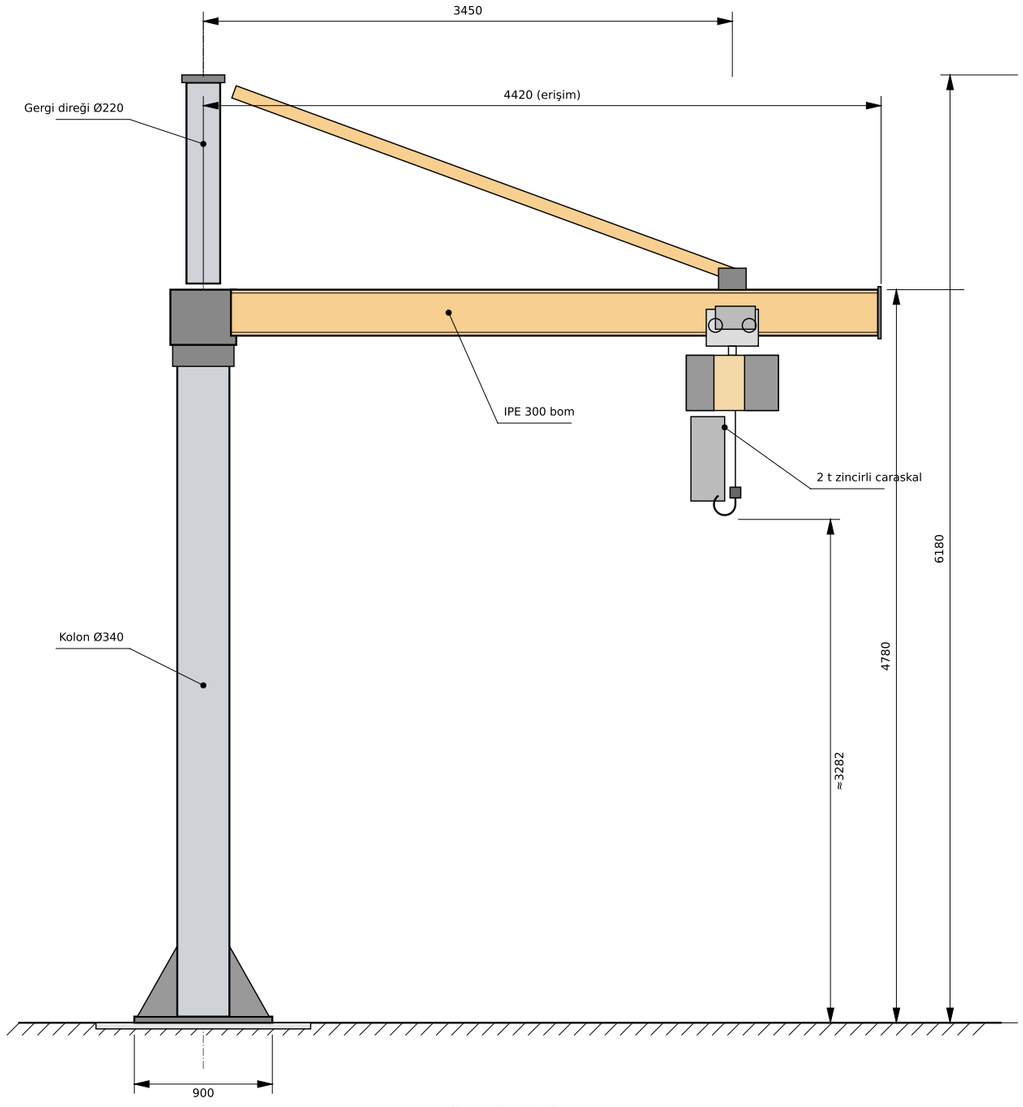


ÖN GÖRÜNÜŞ
Ölçek 1:40

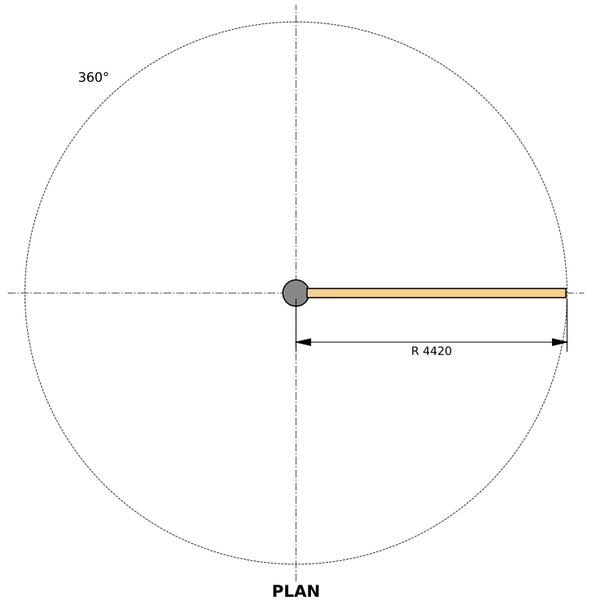

PLAN
Ölçek 1:100

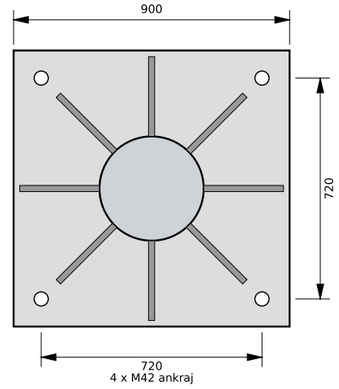

TABAN LEVHASI
Ölçek 1:20

NOTLAR

1. Kolon Ø340 boru (S355JR), taban levhası 900x900x40, 8 guse, 4 ankraj (M42) 720x720 aks.
2. Dönen başlık Ø430, üstünde Ø220 gergi direği; gergi Ø84, bom üst flanşında pimli kulak.
3. Bom IPE 300, üstten gergili; alt flanş caraskal yürüyüş yolu olarak serbesttir.
4. Dönme açısı 360°. Festoon C rayı bom yanında.
5. Temel boyutları zemin etüdüne göre statik projede belirlenir.

beta
VİNÇ SİSTEMLERİ

ÇİZİM ADI: **KOLON TİPİ PERGEL VİNÇ**			
KAPASİTE: **2 t (zincirli caraskal)**			
ÖLÇEK: **1:40 / 1:100 / 1:20**	ÖLÇÜ BİRİMİ: **mm**	TARİH: **18.10.2026**	PAFTA NO: **BV-PV-02**
MALZEME: **S355JR yapı çeliği (taşıyıcılar)**		YÜZEY: **Boya RAL 1028 tonu / RAL 7016**	

Görselleştirme modelinden türetilmiştir. İmalat ve statik hesap için onaylı proje esas alınır.