

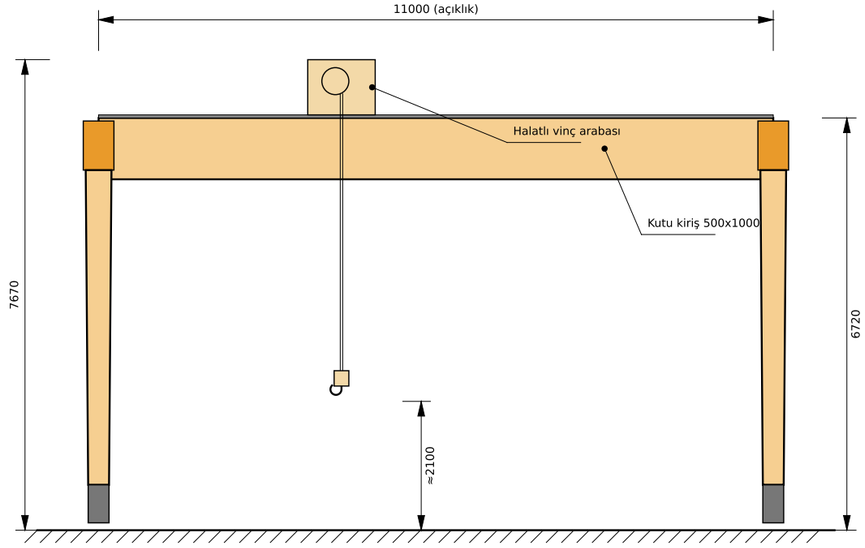


ÖN GÖRÜNÜŞ
Ölçek 1:100

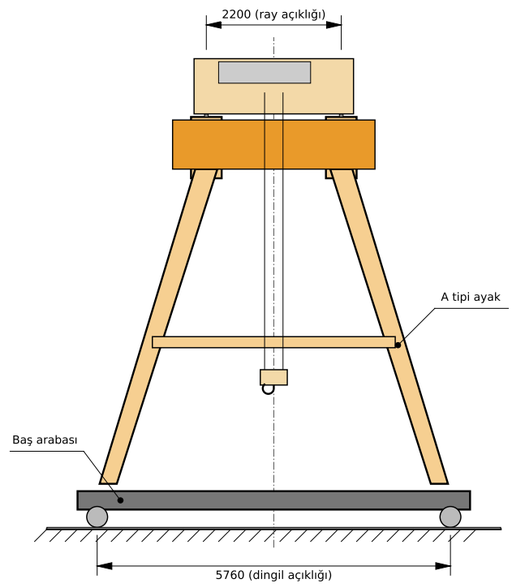

YAN GÖRÜNÜŞ
Ölçek 1:100

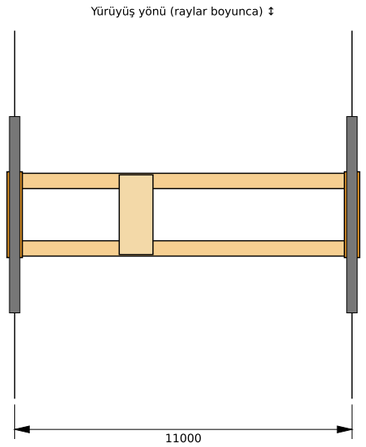

PLAN
Ölçek 1:200

NOTLAR

1. Ana kirişler 2 x kutu kiriş 500x1000 (S355JR), uç kirişlerle alın levhalı cıvatalı birleşim.
2. Her uçta kirişe dik düzlemde A tipi iki ayak; ayak-uç kiriş ve ayak-baş arabası flanşları cıvatalı.
3. Baş arabaları tekerlek bloklu, motor-redüktör-fren tahrikli; raylar kirişe dik doğrultudadır.
4. Halatlı vinç arabası iki kirişin üstündeki raylarda yürür; enerji festoon sistemiyle.
5. Yakın ayakta merdiven ve besleme kablo tamburu; ray sonlarında stoper ve tampon.

beta VİNÇ SİSTEMLERİ	ÇİZİM ADI **ÇİFT KİRİŞLİ PORTAL VİNÇ**		
	KAPASİTE **— (projeye göre)**		
ÖLÇEK **1:100 / 1:200**	ÖLÇÜ BİRİMİ **mm**	TARİH **18.10.2026**	PAFTA NO **BV-PV-03**
MALZEME **S355JR yapı çeliği (taşıyıcılar)**		YÜZEY **Boya RAL 1028 tonu / RAL 7016**	
Görselleştirme modelinden türetilmiştir. İmalat ve statik hesap için onaylı proje esas alınır.			