

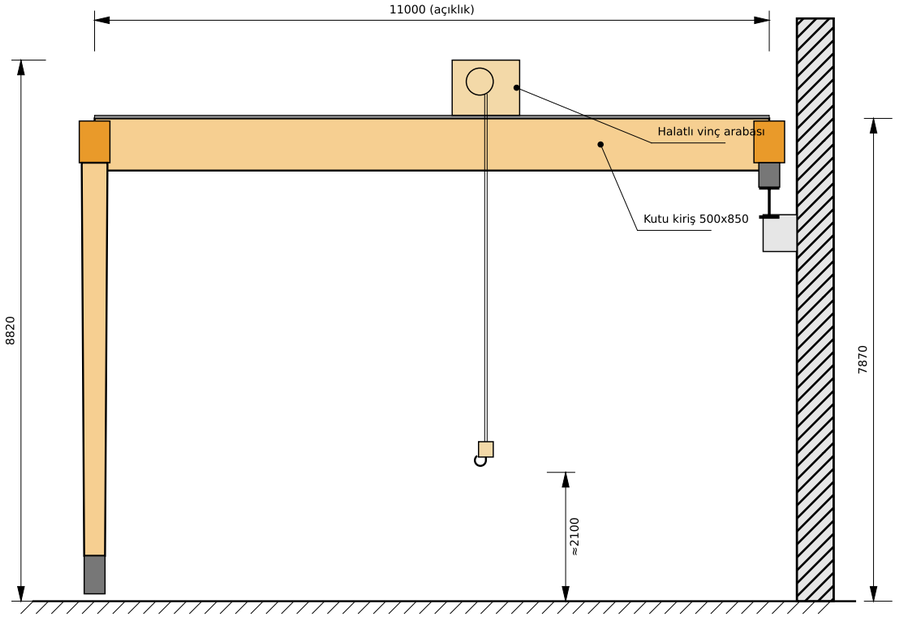


ÖN GÖRÜNÜŞ
Ölçek 1:100

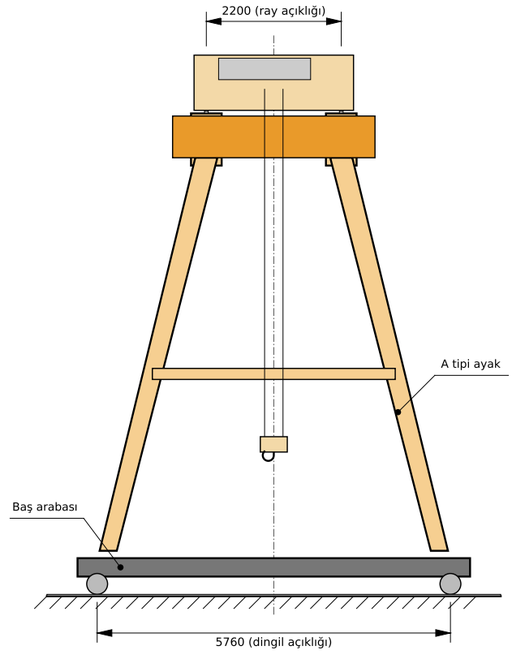

YAN GÖRÜNÜŞ (AYAK TARAFI)
Ölçek 1:100

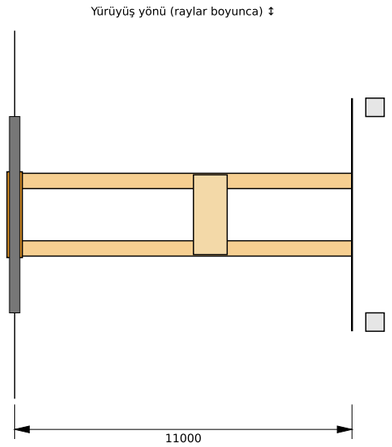

PLAN
Ölçek 1:200

NOTLAR

1. Bir uç A tipi ayaklarla zemin rayında, diğer uç bina kolonu konsolundaki yürüyüş yolu kirişinde.
2. Ana kirişler 2 x kutu kiriş 500x850 (S355JR), uç kirişlerle cıvatalı birleşim.
3. Yürüyüş yolu kirişi bina kolonu konsollarına oturur; kolon ve konsol ölçüleri bina projesinde.
4. Halatlı vinç arabası iki kirişin üstündeki raylarda yürür; enerji festoon sistemiyle.
5. Ray sonlarında stoper ve tampon; ayakta merdiven ve kablo tamburu.

beta VİNÇ SİSTEMLERİ	ÇİZİM ADI **ÇİFT KİRİŞLİ YARI PORTAL VİNÇ**		
	KAPASİTE **— (projeye göre)**		
ÖLÇEK **1:100 / 1:200**	ÖLÇÜ BİRİMİ **mm**	TARİH **18.10.2026**	PAFTA NO **BV-PV-04**
MALZEME **S355JR yapı çeliği (taşıyıcılar)**		YÜZEY **Boya RAL 1028 tonu / RAL 7016**	
Görselleştirme modelinden türetilmiştir. İmalat ve statik hesap için onaylı proje esas alınır.			